(參考圖1－1)

有騎樓無人行道(剖面圖)

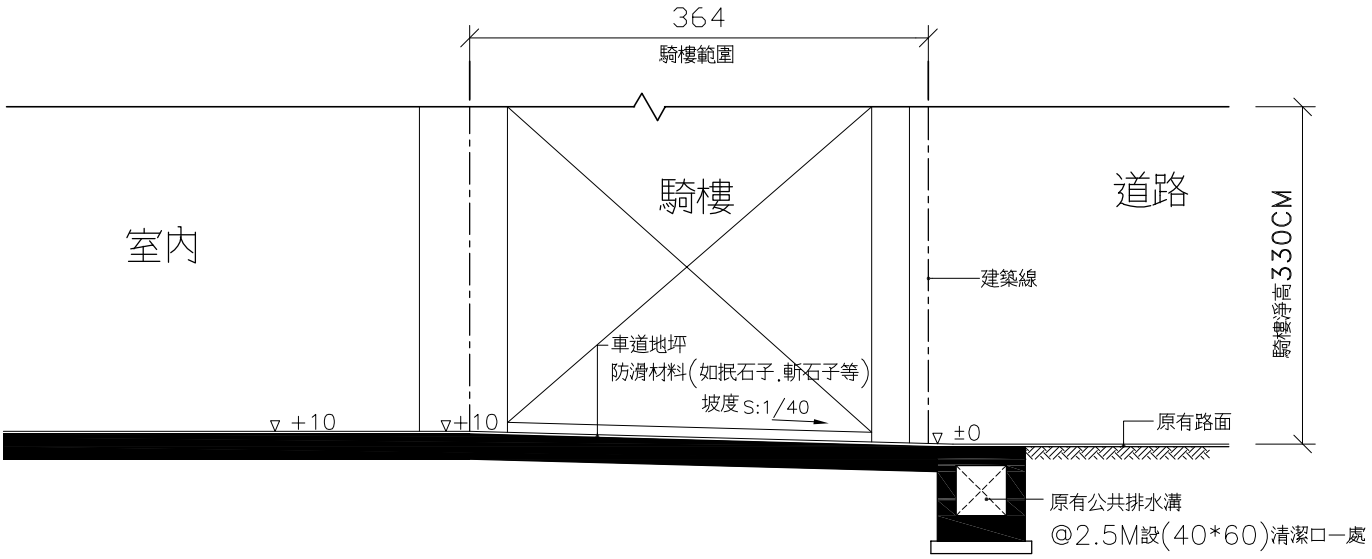

Ⓐ 車道出入口剖面詳圖

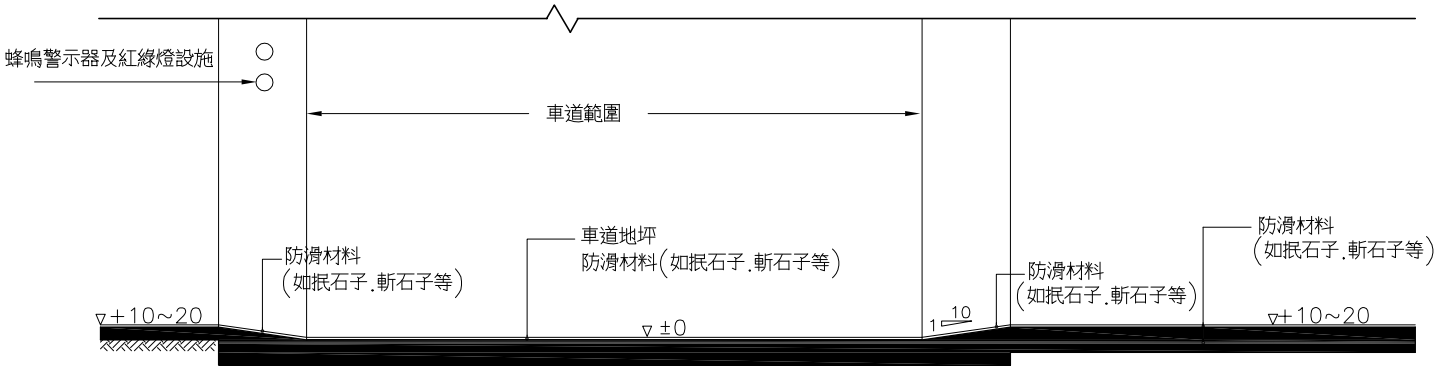

Ⓑ 車道出入口剖面詳圖